
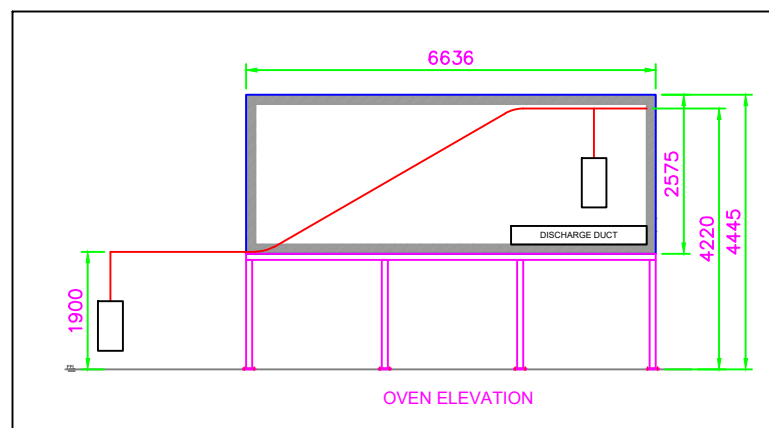
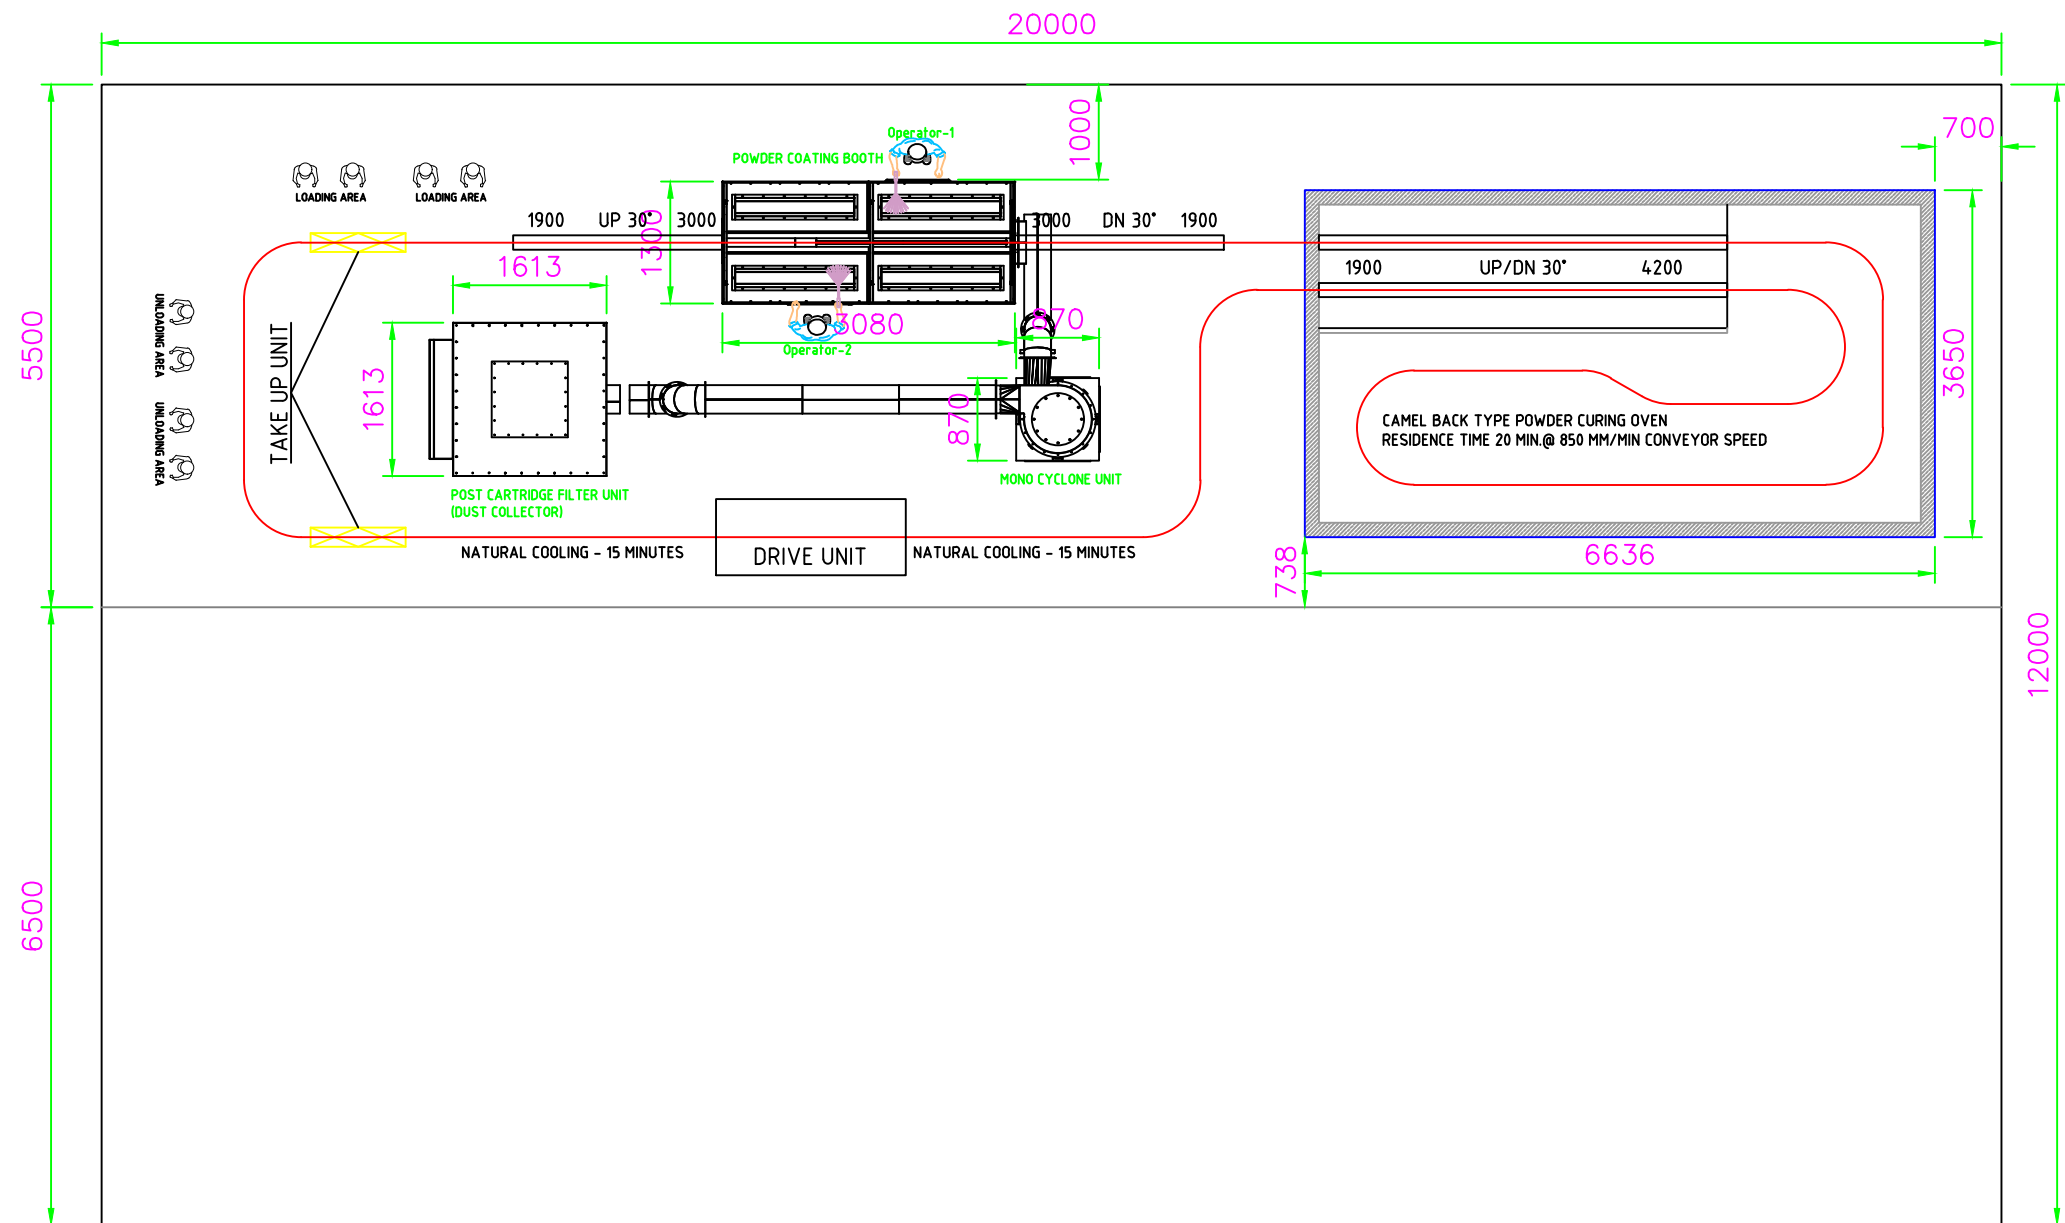


- CONVEYOR DETAILS--:**
1. CONVEYOR SPEED - 800 ~ 1000 MM/MIN.
 2. CONVEYOR TYPE - CLOSE TRACK
 3. HANGING PITCH - 200 MM.
 4. COMPONENT PITCH - 600 MM.
 5. CONVEYOR LENGTH - 60 ~ 65 MTR. APPROX.

- REMARKS--:**
1. ALL DIMENSIONS ARE IN MM.
 2. IF ANY DOUBT, PLEASE ASK.
 3. THIS IS A GENERAL ARRANGEMENT DRAWING.
(SUBJECT TO CHANGE)

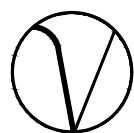

MFG.
VALUE ADDED COATING SOLUTION P. LTD.
515, DEVIKA TOWER CHANDRA NAGAR GHAZIABAD (U.P)
MOB : +91 9319086612
Email : SALES@OPTIFINISH.IN

PROJECT NAME: POWDER COATING PLANT
TITLE NAME: GENERAL ARRANGEMENT DWG.
DATE : 25.06.2024

CLIENT NAME: M/S M.R. TUBES

DESCRIPTION:

DRAWN BY

CHKD BY

APPROVED BY

DRAWING NO.

SHEET NO.

REVISION NO.

REVISION NO.

REVISION NO.