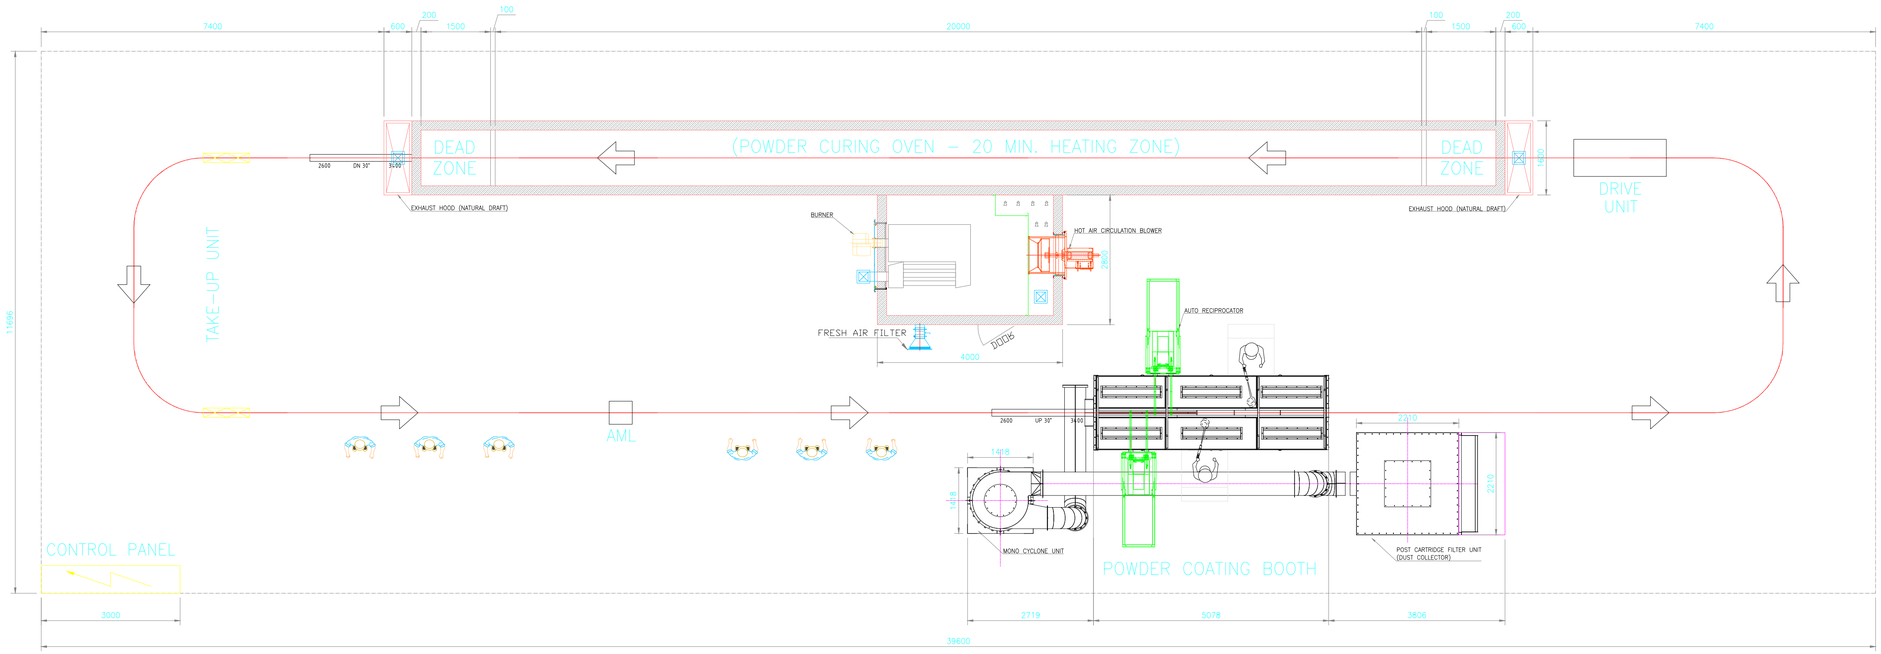

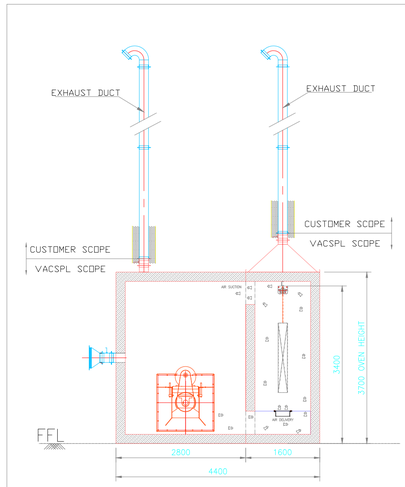

CROSS SECTION FOR WDO

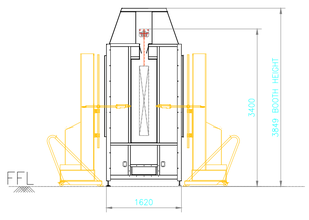

CROSS SECTION FOR BOOTH

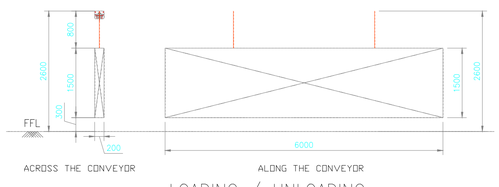

ACROSS THE CONVEYOR

ALONG THE CONVEYOR

LOADING / UNLOADING

THE COPYRIGHT OF THESE DRAWINGS AND OF ALL ENCLOSURES ENTRUSTED TO THE RECIPIENT PERSONALLY REMAINS THE EXCLUSIVE PROPERTY OF THIS FIRM, WITHOUT OUR WRITTEN CONSENT THEY MAY NOT BE COPIED OR REPRODUCED OR DELIVERED OR MADE KNOWN TO THIRD PARTIES.

- IF IN DOUBT ASK.
- NO. IN TRIANGLE DENOTES ALTERATION
- WORK TO THE DIMENSIONS.
- BREAK SHARP EDGES
- DIMENSIONS ARE IN MM

REV. NO.	ZONE	DESCRIPTION	MADE BY DATE	CHKD APPD

REV. NO.	ZONE	DESCRIPTION	MADE BY DATE	CHKD APPD

NOTES:

1) CONVEYOR SPEED 1.0 Mtr/Min.
2) COMPONENT ENVELOPE SIZE IN mm – 6000L x 200W x 1500H
3) CONVEYOR HORIZONTAL RADIUS – 1500mm.
4) CONVEYOR LENGTH – 85 Meters.
5) THIS IS A GENERAL ARRANGEMENT DRAWING.(SUBJECT TO CHANGE)

CLIENT: SARKAR ENTERPRISES, KOLKATA

REPLACED BY FOR

TITLE: **LAYOUT FOR POWDER COATING PLANT**

SCALE: 1:65

DRAWN	L	13.10.2024
DESIGNED		
CHECKED		
APPROVED		

MFG.
VALUE ADDED COATING SOLUTION P. LTD.
515,DEVIKA TOWER CHANDRA NAGAR GHAZIABAD (UP)
MOB : +91 9319086612
Email : SALES@OPTIFINISH.IN

O.C. NO. 00

DRG. NO. 00 00 00 00 00

REV. NO. 0